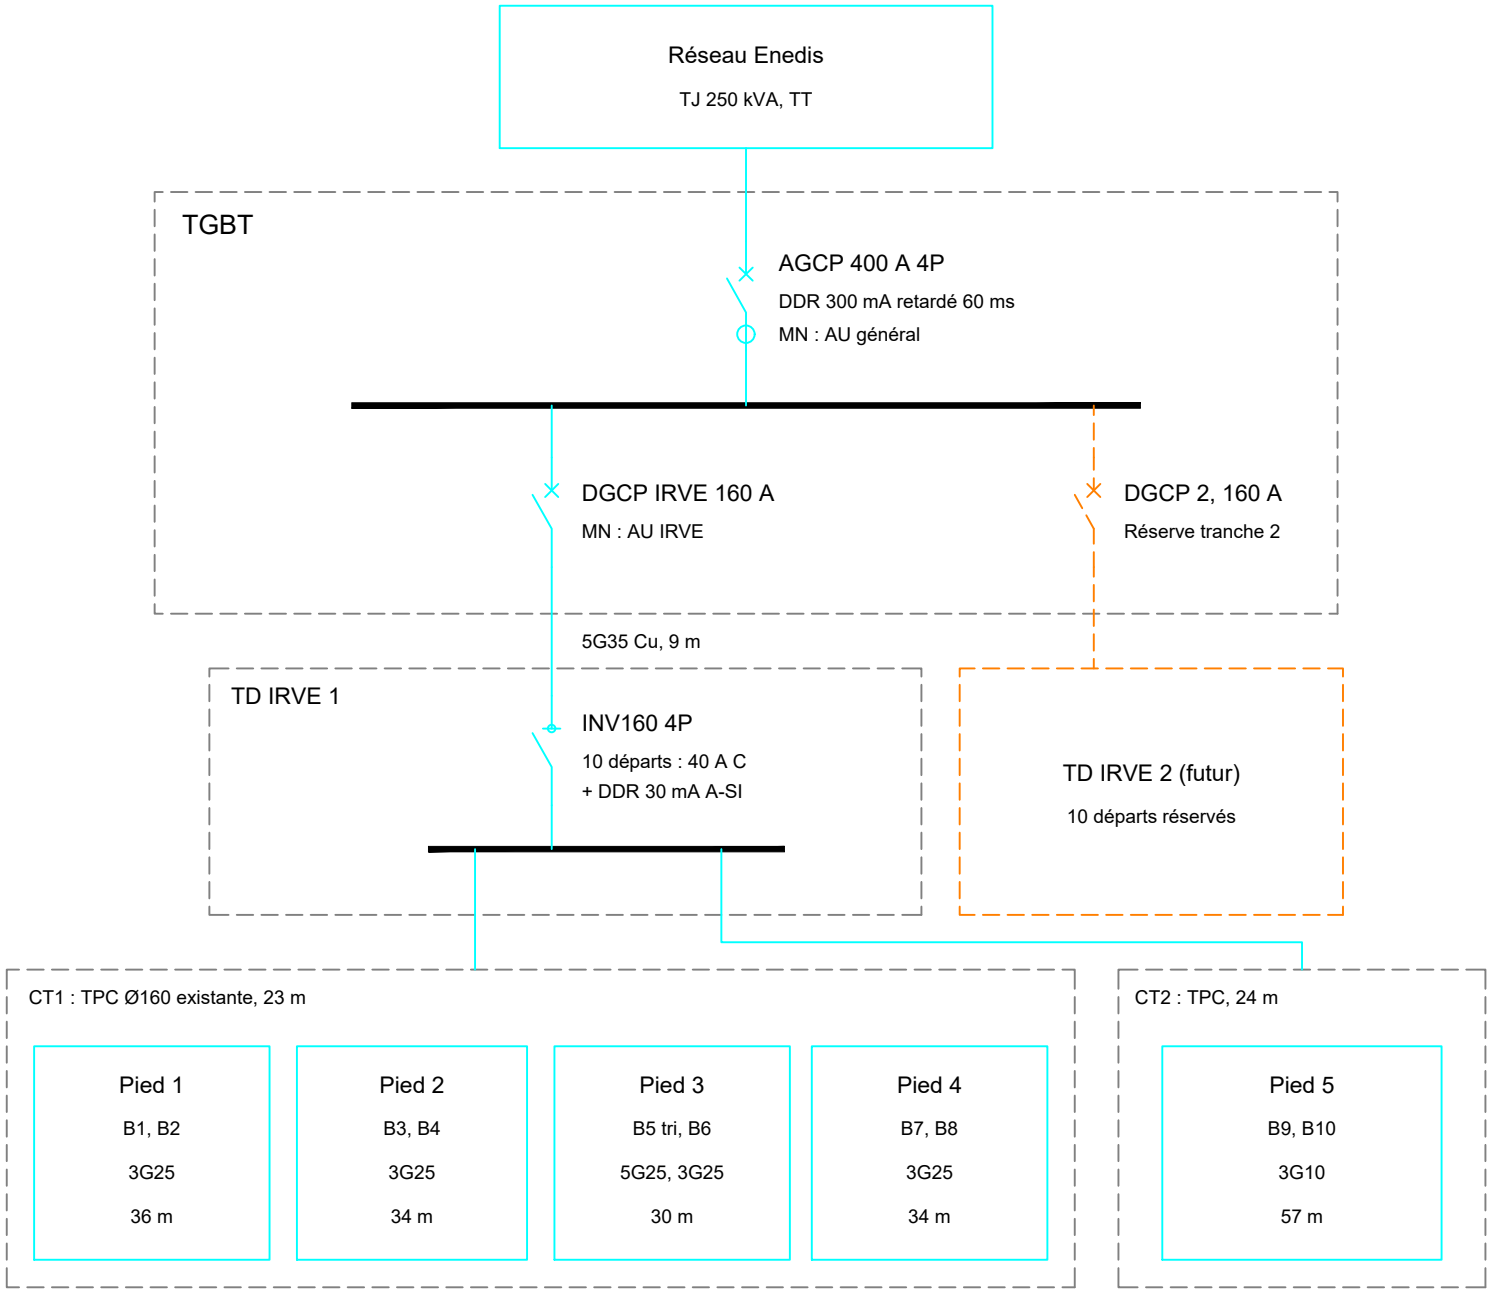


Légende

- Disjoncteur
- Disjoncteur + DDR
- Interrupteur-sectionneur

Pointillés : tranche 2, extension à 20 bornes (second départ identique)

Terre IRVE dédiée, pieds reliés au réseau équipotentiel

COS PHIPHI INGÉNIERIE
Domaine du Grand Ampère
Création IRVE 10 bornes
SCHÉMA DE PRINCIPE
Indice A - 13/10/2026
Dessiné : D. HAOUCHE - A3 sans échelle